
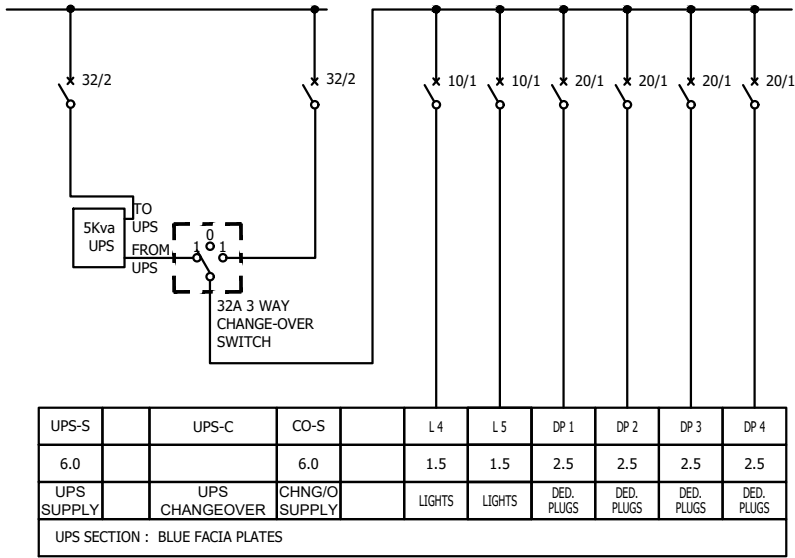


DB-FO

DISTRIBUTION BOARD INFORMATION				
CONSTRUCTION	YES	NO	LIMITING DIMENSIONS	
RECESSED			WIDTH:	MOS
SEMI-RECESSED	X		HEIGHT:	MOS
SURFACE			DEPTH:	MOS
FREE STANDING			COLOR SABS 1081	
FLOOR STANDING			STANDBY SECTION (E)	WHITE FACIA
DOORS			UPS SECTION (U)	BLUE FACIA
DOORS LOCKABLE	X		ISOLATED TX SECTION (IS)	WHITE FACIA
SEPARATE CUBICLES				
Spare Space	35%	%	VOLTAGE:	400 VOLT
SERVICE ACCESS	FRONT:	X	REAR:	BOTH:
ENTRY:	TOP:	X	BOTTOM:	SIDE:
INCOMING:		X		
OUTGOING:		X		X
BUSBAR RATING	RATING (N)		RATING (E)	FAULT LEVEL
PHASE	3 PHASE	80		5 KA
BUSBAR NEUTRAL			HALF:	FULL: X

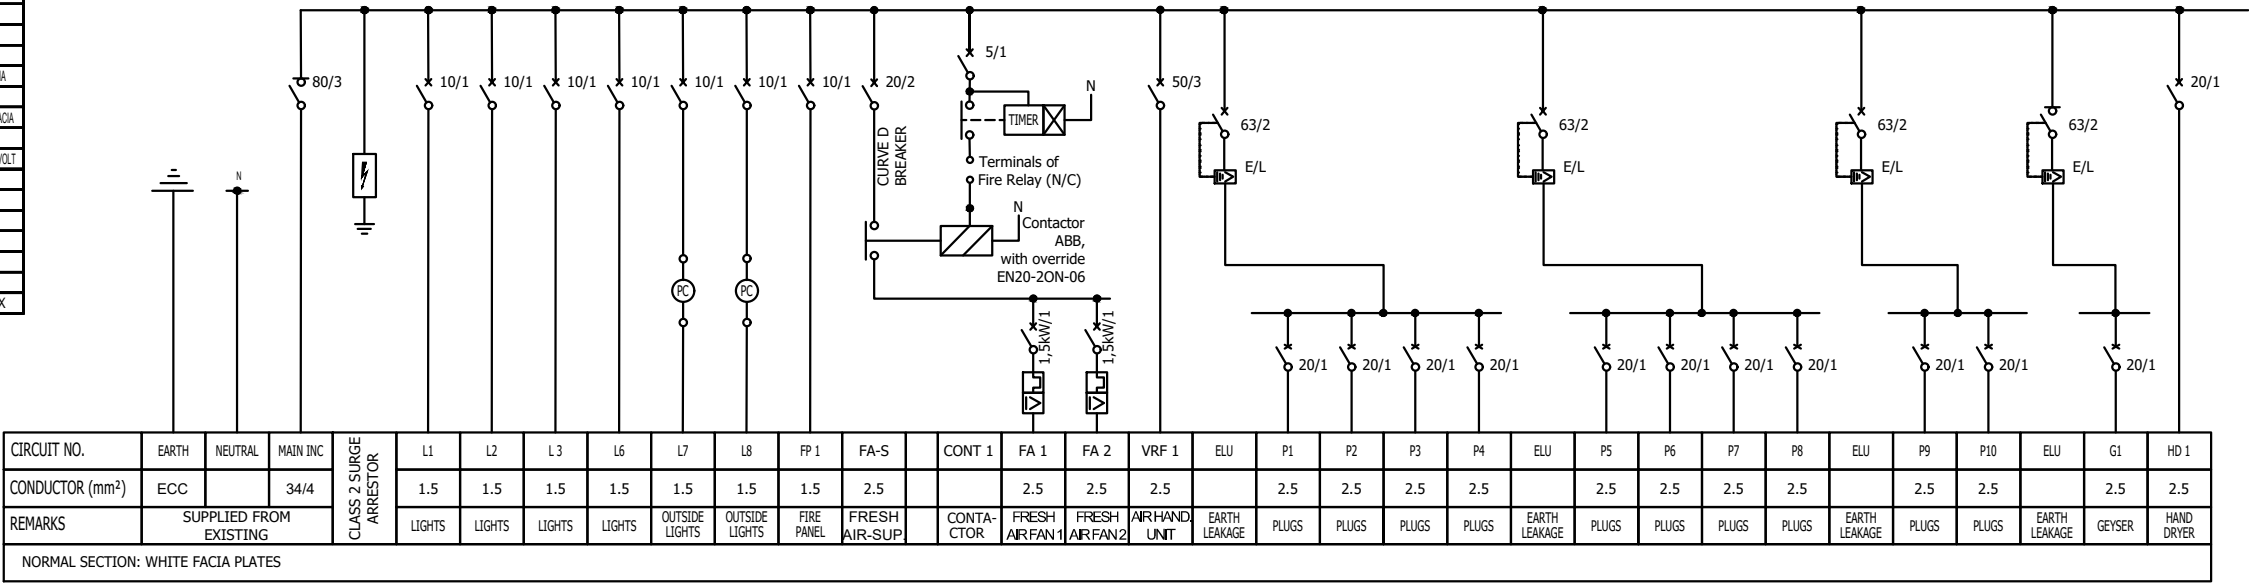

SHEET SIZE

A3

REV	DATE	DESCRIPTION
A	2025/12/15	ISSUED FOR TENDER

NOTE:
ALL MEASUREMENTS TO BE CHECKED ON SITE.
IF IN DOUBT, ASK.
THIS DESIGN & DRAWING IS THE INTELLECTUAL & CONFIDENTIAL PROPERTY OF **CA du Toit EC (PTY) LTD** AND MAY NOT BE DISCLOSED TO THIRD PARTY, COPIED OR REPRODUCED IN WHOLE OR IN PART WITHOUT THE PERMISSION OF **CA du Toit EC (PTY) LTD**.

CAduToit
CONSULTING ENGINEERS / RAADGEWENDE INGENIEURS

Eastern Cape (Pty) Ltd
22 Shirley Street
Newton Park
Gqeberha
6045

E-mail
pe@caoutotec.co.za
Telephone
+27 (0)41 585 7559

PROJECT:
FORT HARE UNIVERSITY FINANCE OFFICES
DRAWING:
DISTRIBUTION BOARD LAYOUT

SCALE:	DATE:
N. T. S.	2025/12/15
DRAWN:	DESIGNED:
C. CLAASEN	P. STRYDOM
APPROVED:	VERIFIED:
P. STRYDOM	L. BRIGHT

ISSUED FOR:
TENDER

CONSULTANTS JOB REFERENCE NUMBER.	
P8080E01-003	
SHEET NO:	REV. NO: A