


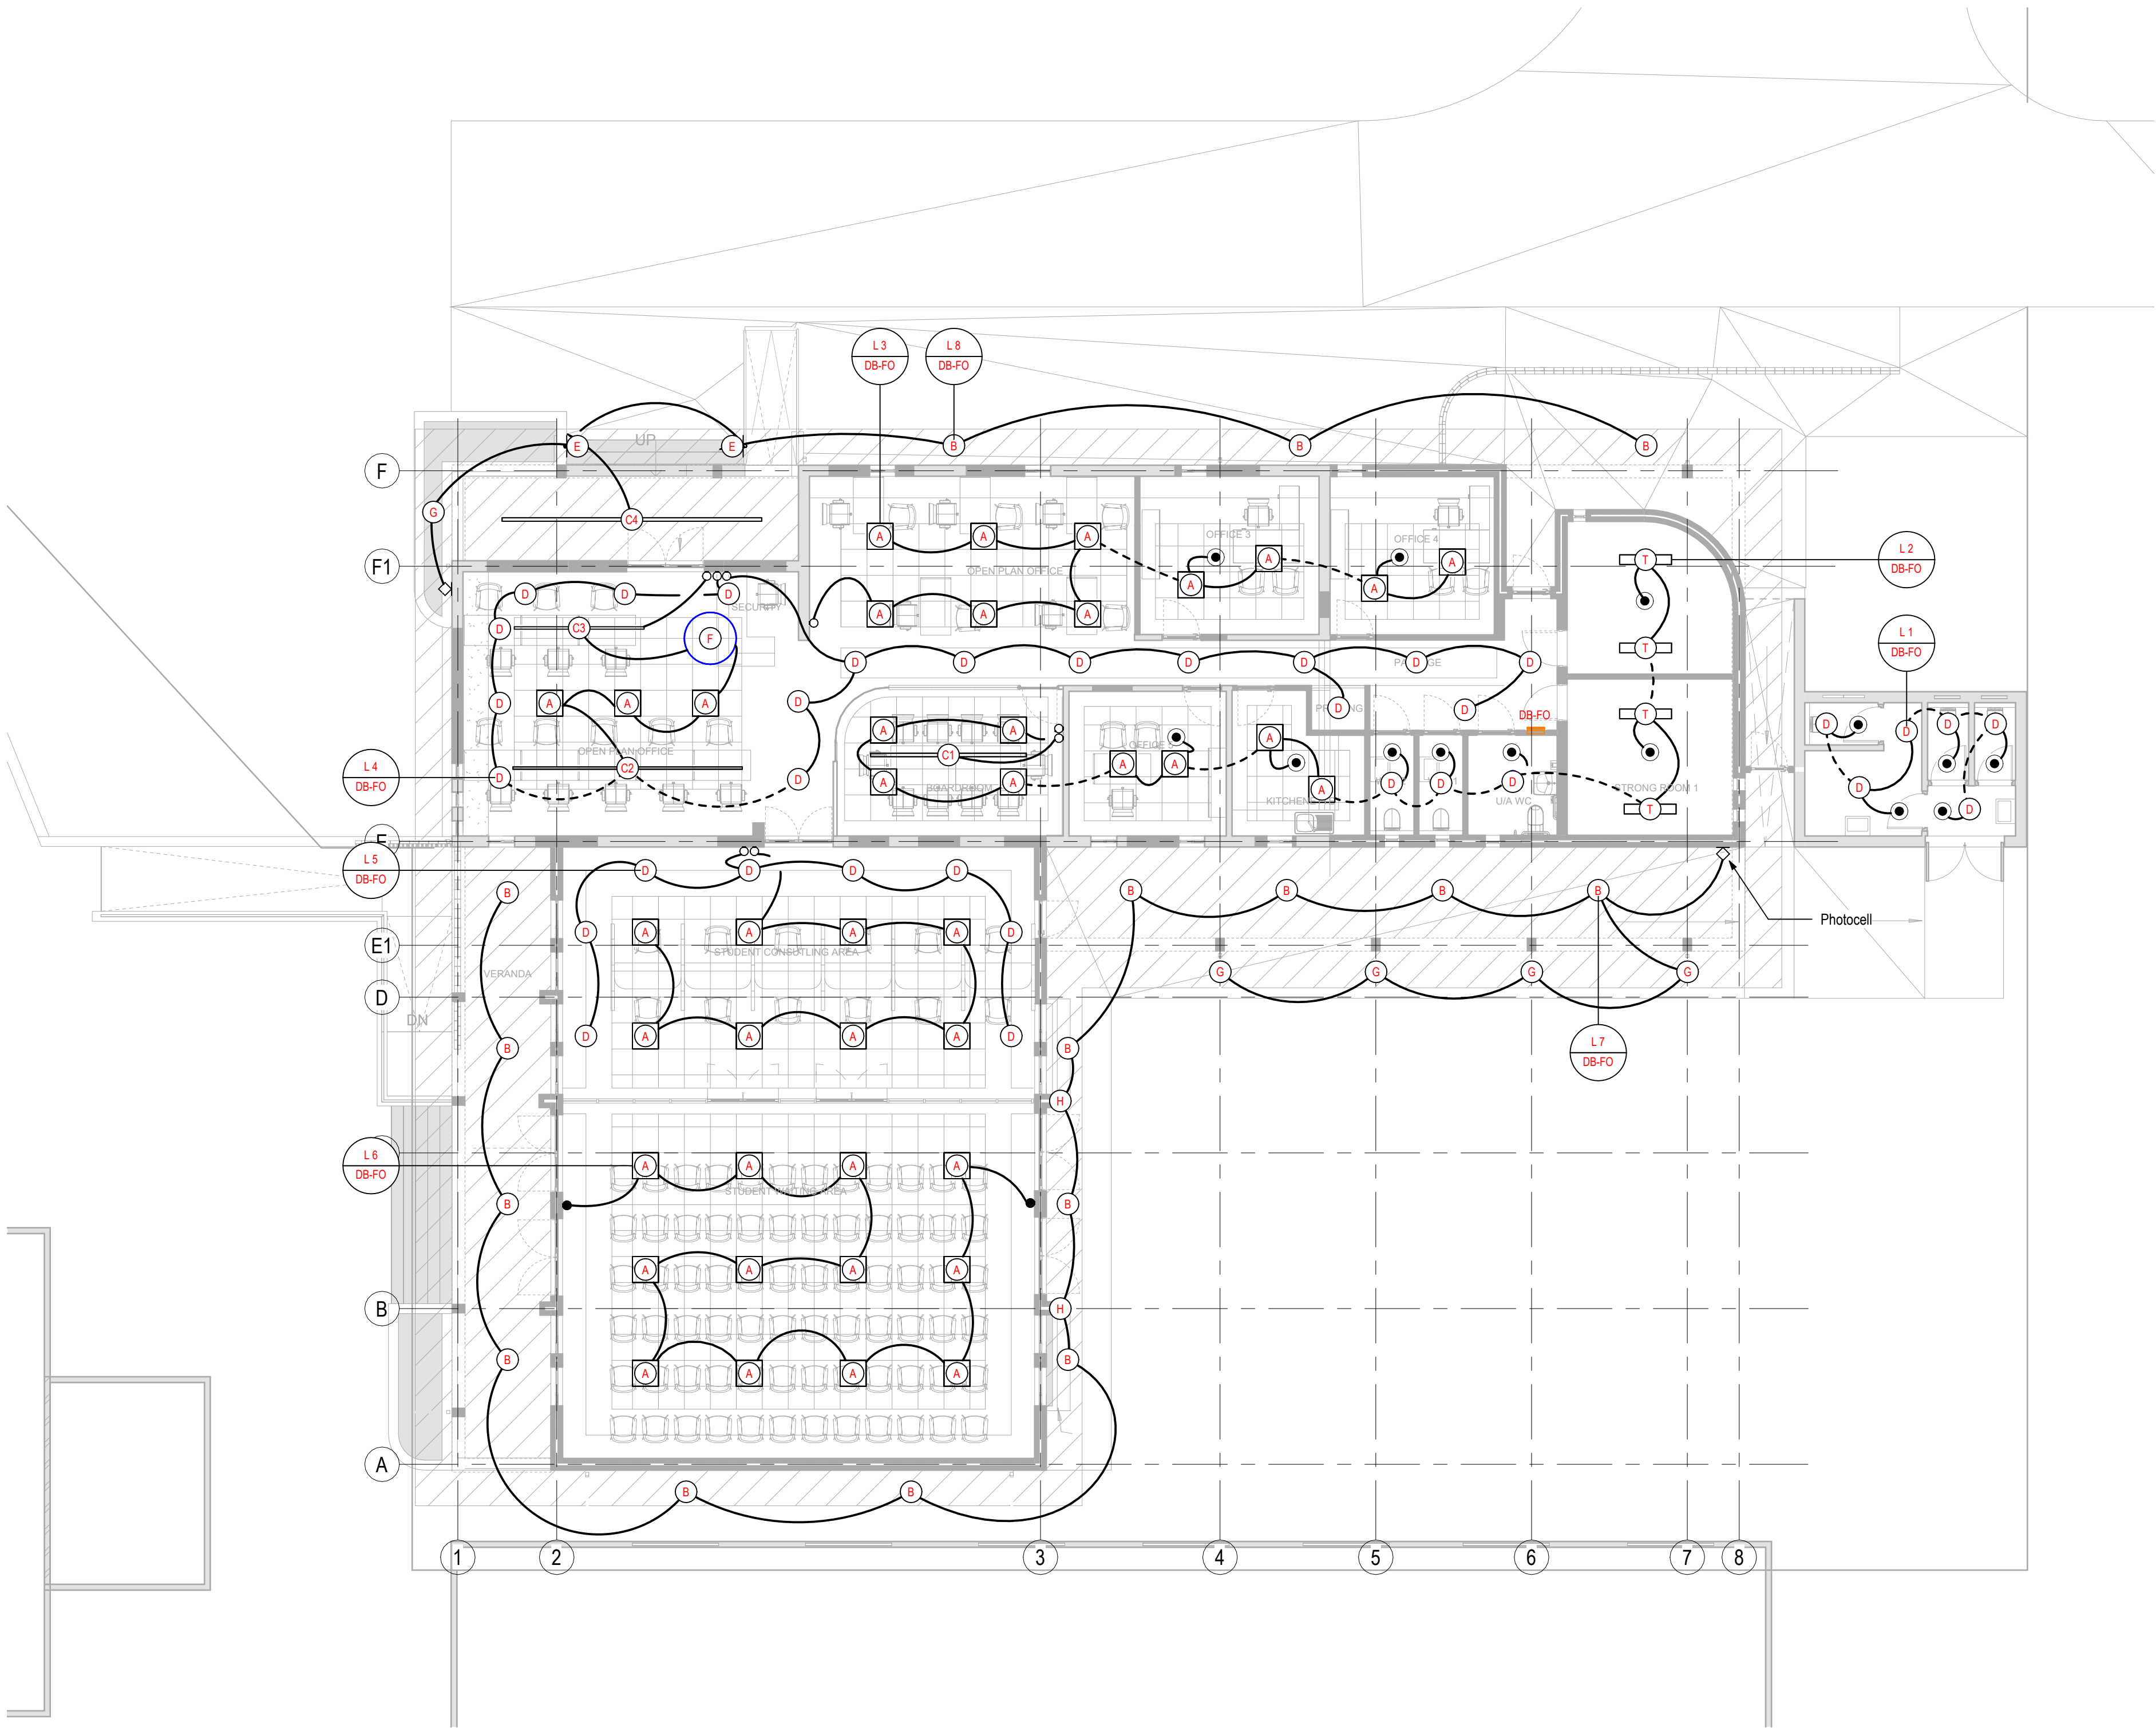

GROUND FLOOR LIGHTING

1 : 100

LEGEND	
	DISTRIBUTION BOARD
	DUO 16A SSO - 1xOld Type 1xNew Type
	SET ON OUTLETS IN POWER SKIRTING CONSISTING OF: 1 x OLD RSA SSO, 1 x NEW RSA SSO(EURO), 2xDED SSO, 2xRJ45 OUTLETS & COMBO SOCKET OUTLET
	SET ON OUTLETS IN POWER SKIRTING CONSISTING OF: 1xOLD RSA SSO, 1xNEW RSA SSO(EURO), 2xDED SSO, 1xUSB & 2xRJ45 OUTLETS
	FLOOR MOUNTED PEDESTAL PLUG COMPLETE WITH: 1xOLD RSA SSO 1xNEW RSA SSO(EURO)
	DATA POINT (RJ45)
POWER SKIRTING, 2 TIER, PVC, COMPLETE WITH BENDS AND END CAPS AS REQUIRED, TO BE MOUNTED AT HEIGHTS AS PER THE ARCHITECTS DETAIL TO SUITE JOINERY.	
LUMINAIRES	
	REC - 600x600 - 2 CELL DIFFUSER
	ROUND BULKHEAD, BLACK, 15 W
	55w x 80h LINEAR LIGHT, ±3.6m LONG
	55w x 80h LINEAR LIGHT, ±5.4m LONG
	55w x 80h LINEAR LIGHT, ±3m LONG
	55w x 80h LINEAR LIGHT, ±6m LONG
	DOWNLIGHT, RECESSED
	FOOTLIGHT, ± 2W
	Ø1200mm ROUND LED
	UPLIGHT GU10 FITTING
	COLOUR TEMPERATURE LED FLOOD LIGHT
	SPLASH PROOF LED FITTING
	LIGHT SWITCH, 16A, 1 WAY
	LIGHT SWITCH, 16A, 2WAY
	MOTION/PRESENCE DETECTOR
	PHOTOCELL, DAYLIGHT SWITCH

No.	Date	Description
A	2025/11/10	Revised lighting to architect comments.
B	2025/12/12	ADDED CIRCUITS
C	2025/12/15	ISSUED FOR TENDER

NOTE:
ALL MEASUREMENTS TO BE CHECKED ON SITE.
IF IN DOUBT, ASK.
THIS DESIGN & DRAWING IS THE INTELLECTUAL & CONFIDENTIAL PROPERTY OF CA du Toit EC (PTY) LTD AND MAY NOT BE DISCLOSED TO THIRD PARTY, COPIED OR REPRODUCED IN WHOLE OR IN PART WITHOUT THE PERMISSION OF CA du Toit EC (PTY) LTD.

CAduToit Eastern Cape (Pty) Ltd
CONSULTING ENGINEERS / RAADGEWENDE INGENIEURS
22 Shirley Street
Newton Park
GOEBERHA
6045
E-mail
pe@cadutoitec.co.za
Telephone
+27 (0)41 585 7559

PROJECT	FORT HARE UNIVERSITY FINANCE OFFICES
DRAWING	ELECTRICAL INSTALLATION LIGHTING LAYOUT

SCALE (on A1):	DATE:
1 : 100	JULY 2025
DRAWN:	DESIGNED:
C. CLAASEN	L. BRIGHT
APPROVED:	VERIFIED:
L. BRIGHT	P. STRYDOM

ISSUED FOR:	TENDER
-------------	--------

DRAWING NUMBER:	Project Ref:	P8099E01
P8099E01-002	Revision No.:	C