



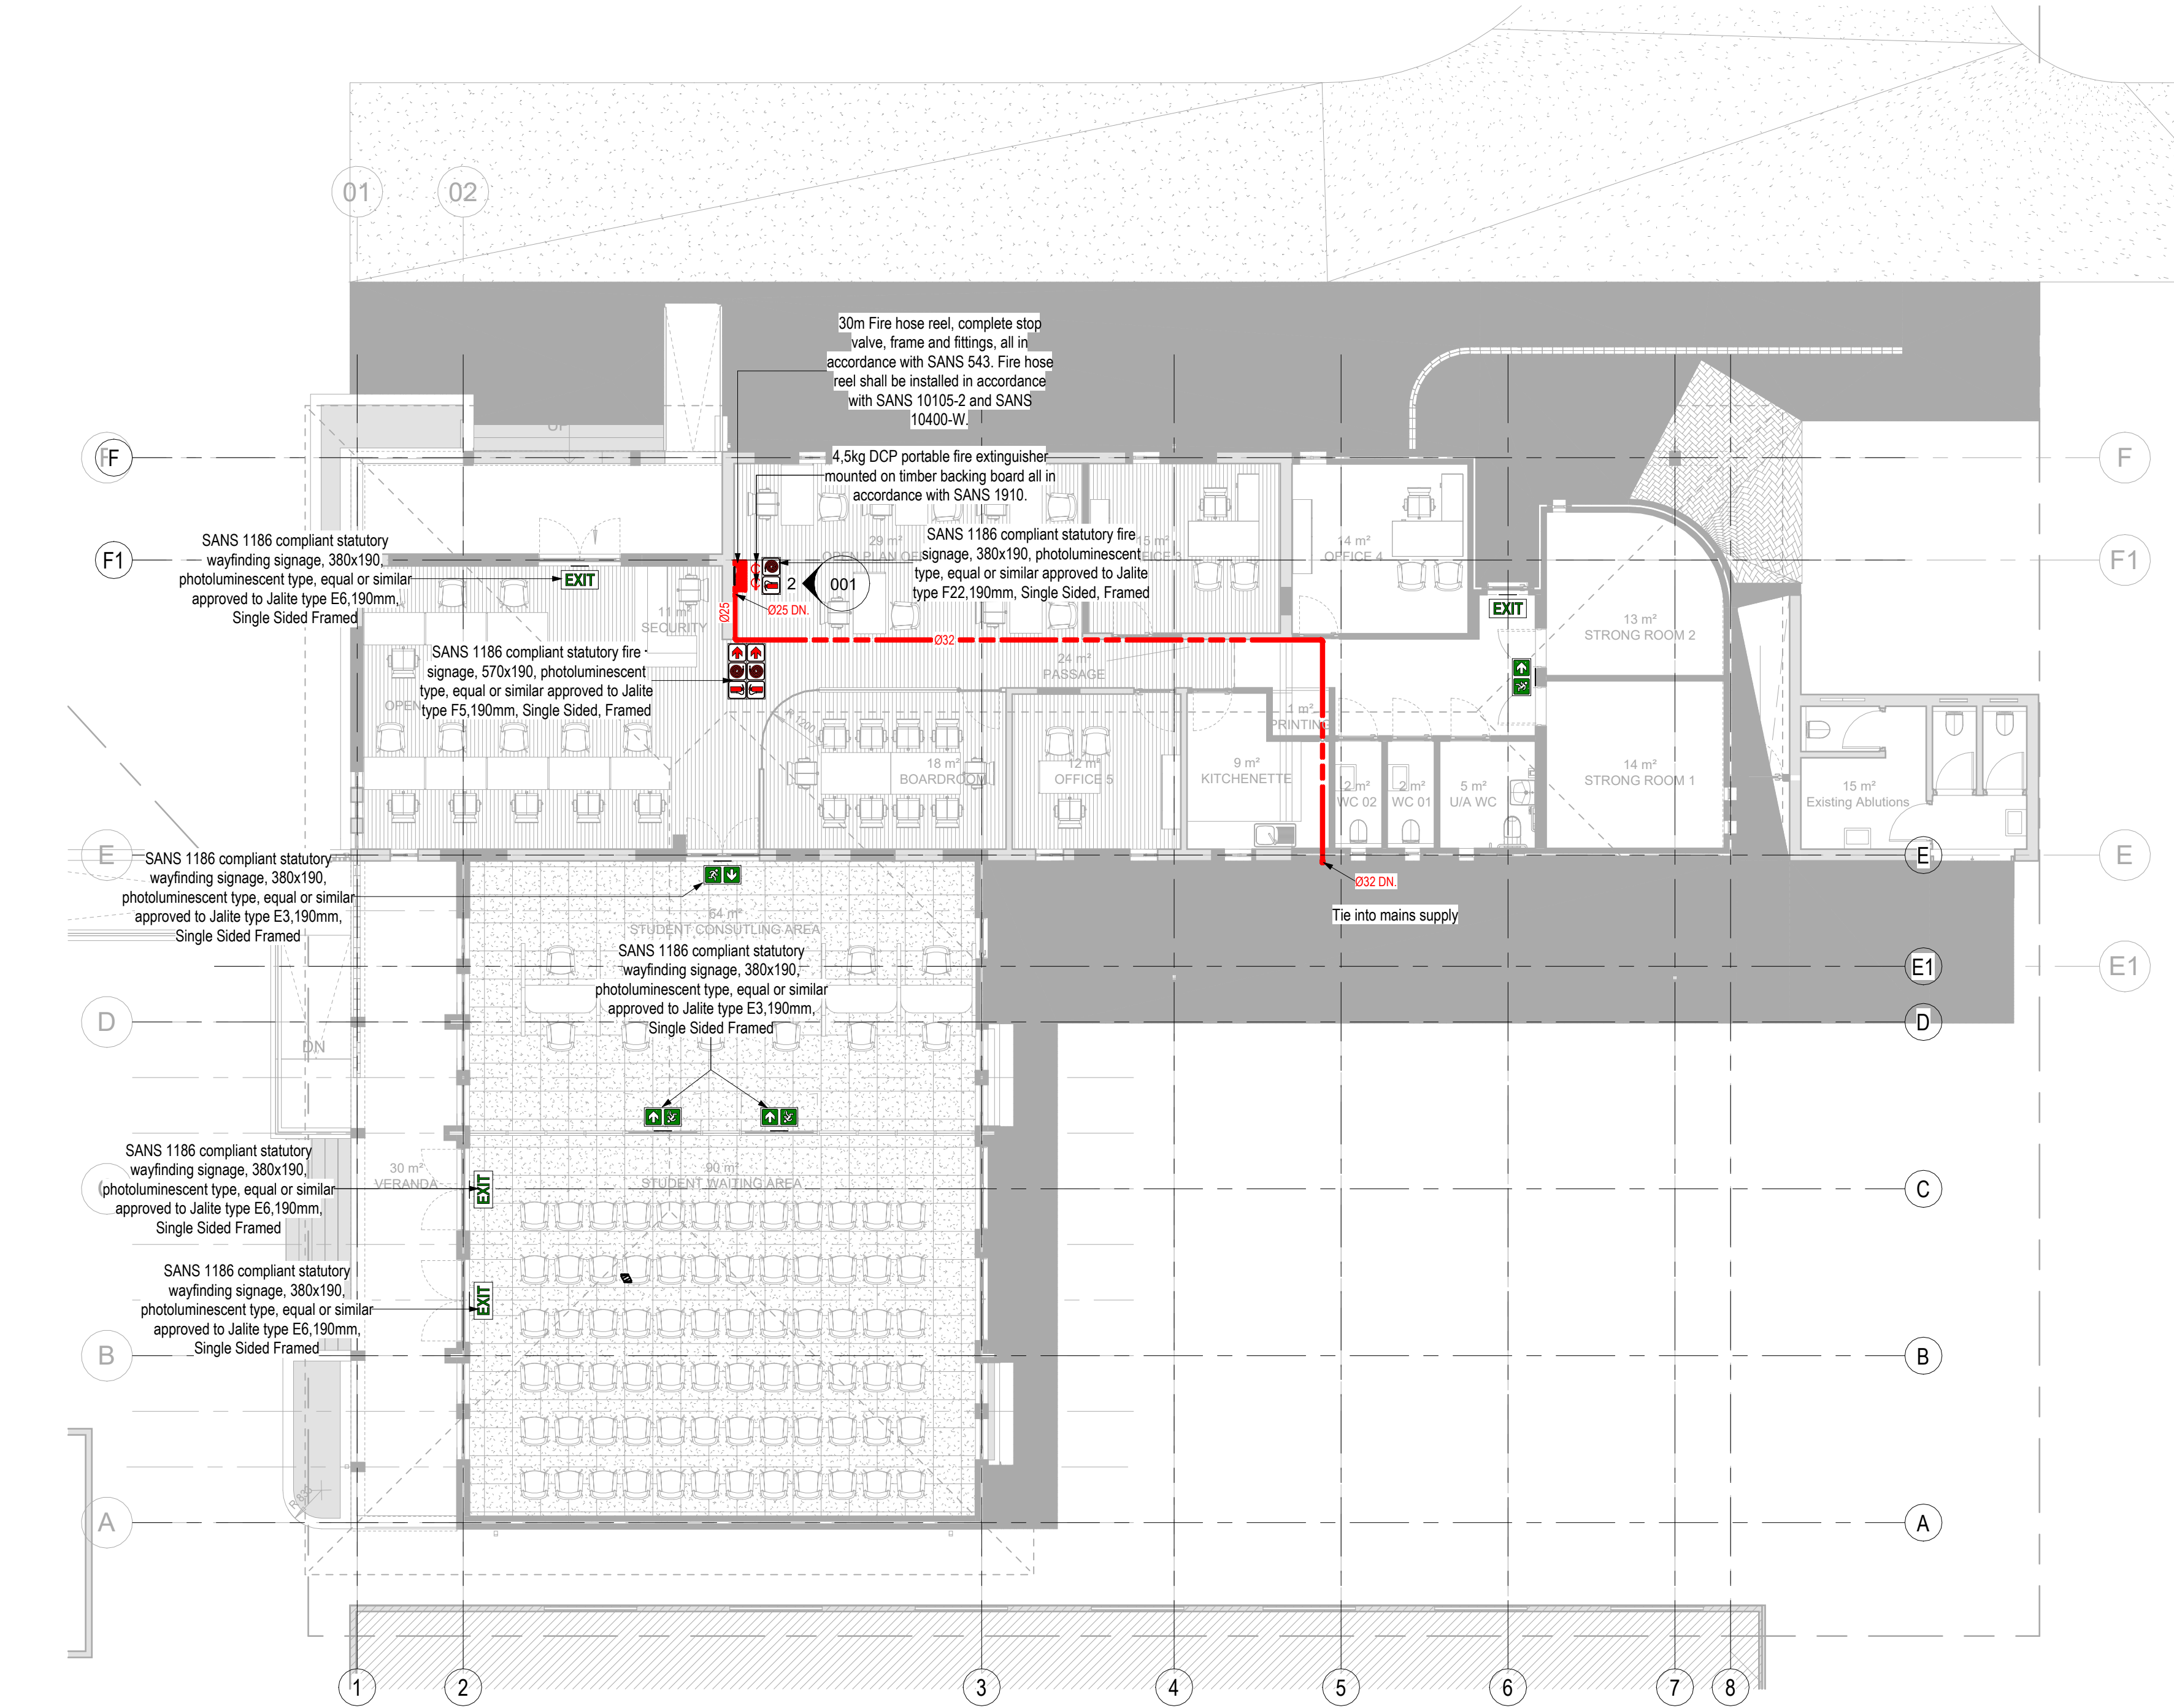

1 GROUND FLOOR
1 : 100

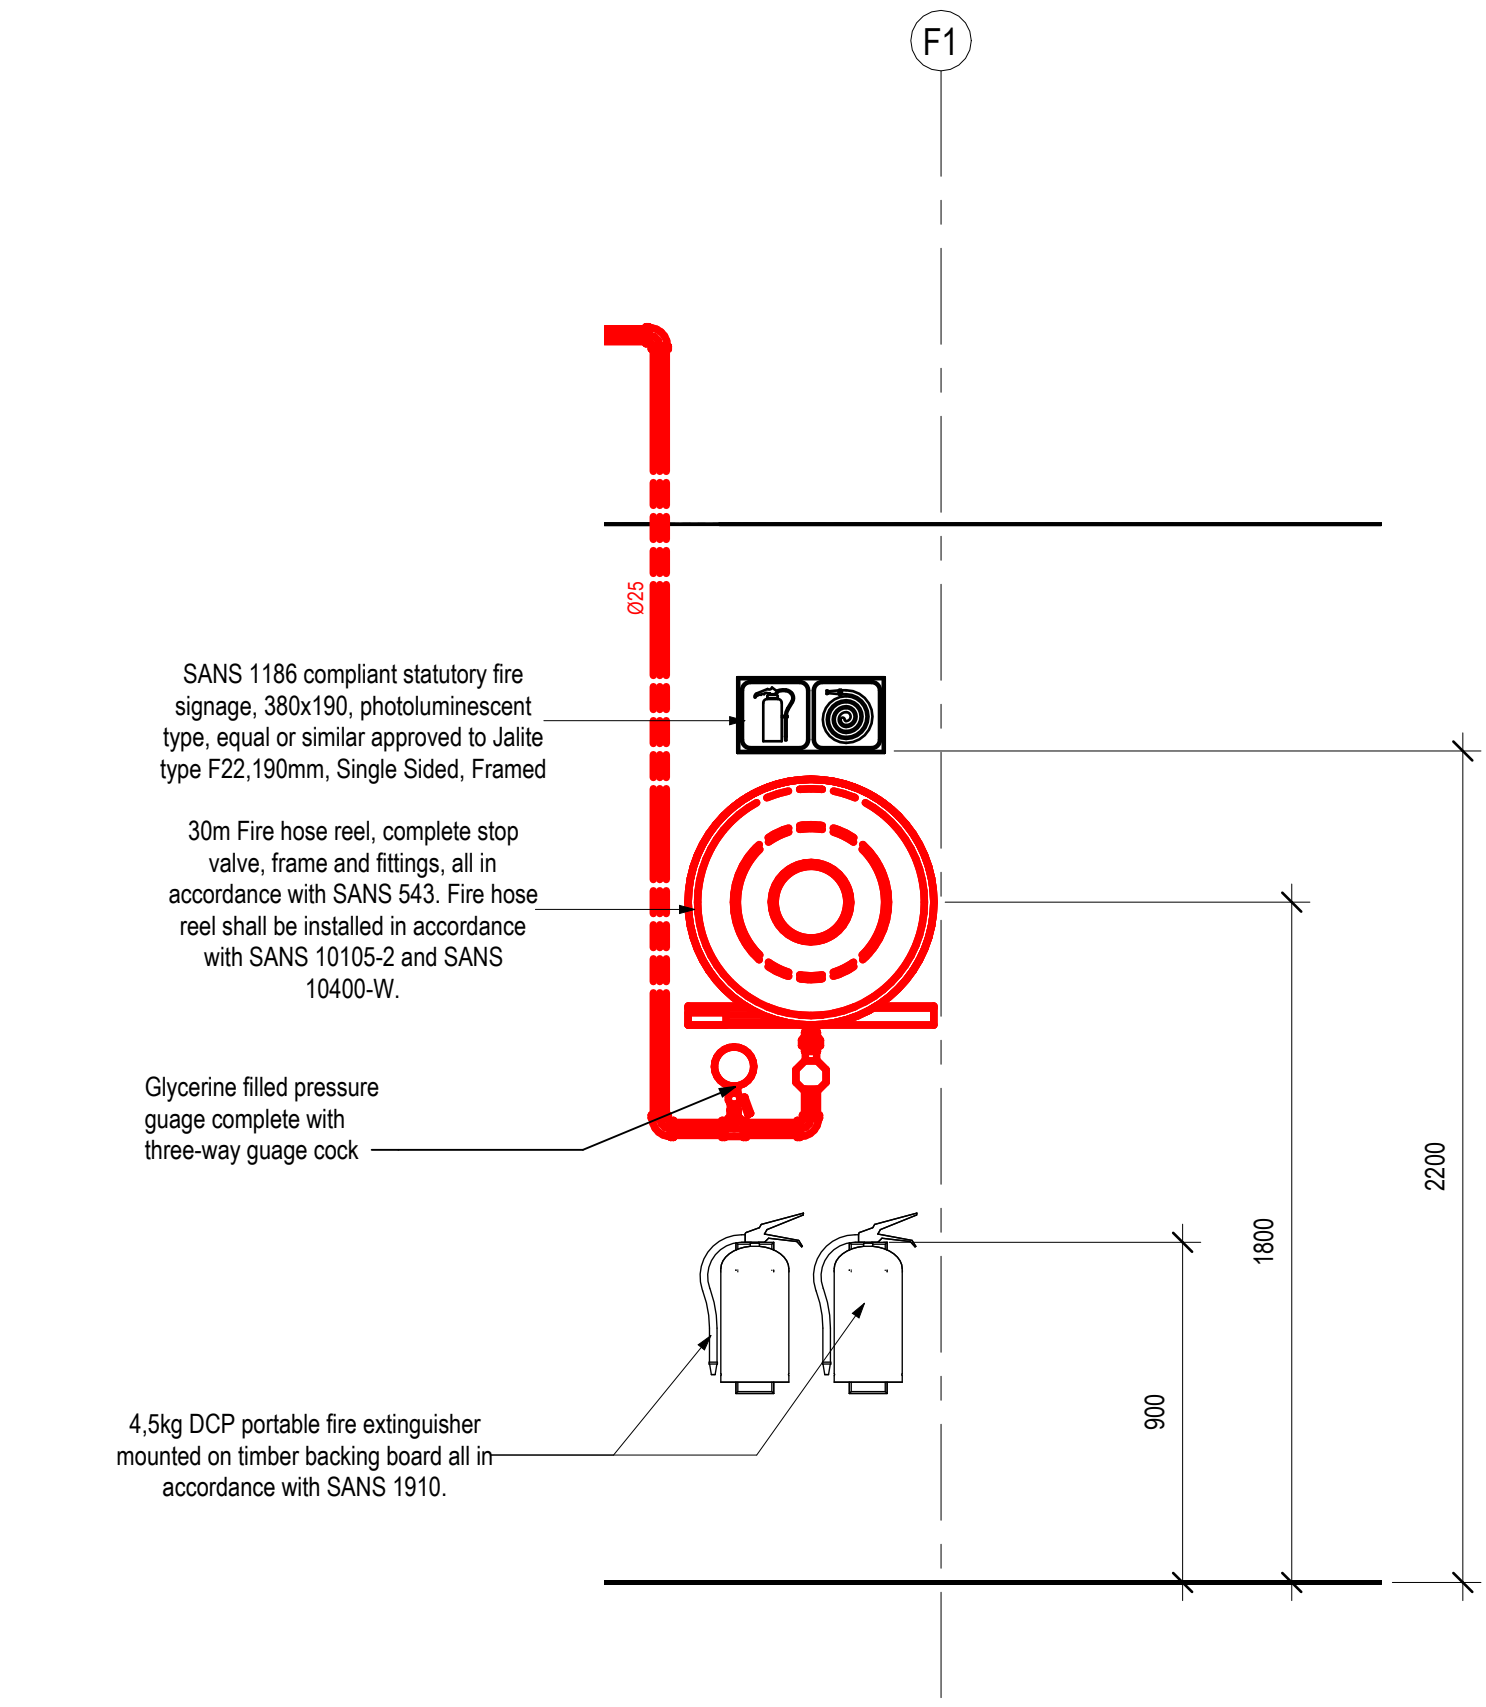

2 Elevation 1 - a
1 : 20

No.	Date	Description
A	2025/12/15	Issued for Tender

NOTE:
ALL MEASUREMENTS TO BE CHECKED ON SITE.
IF IN DOUBT, ASK.
THIS DESIGN & DRAWING IS THE INTELLECTUAL & CONFIDENTIAL PROPERTY OF CA du Toit EC (PTY) LTD AND MAY NOT BE DISCLOSED TO THIRD PARTY, COPIED OR REPRODUCED IN WHOLE OR IN PART WITHOUT THE PERMISSION OF CA du Toit EC (PTY) LTD.

CAduToit Eastern Cape (Pty) Ltd
CONSULTING ENGINEERS / RAADGEWENDE INGENIEURS
22 Shirley Street
Newton Park
GOEBERHA
6045
E-mail
pe@cadutoilec.co.za
Telephone
+27 (0)41 585 7559

PROJECT:	University of Fort Hare - Alice Campus UFH - Alice Campus Finance Offices Conversion
DRAWING:	FIRE PROTECTION INSTALLATION FIRE AND WAYFINDING LAYOUT

SCALE (on A1):	DATE:
As indicated	2025/10/20
DRAWN:	DESIGNED:
A. BROWN	A. BROWN
APPROVED:	VERIFIED:
	A. STRAUSS

ISSUED FOR:
TENDER

DRAWING NUMBER:	Project Ref:	P8080M07
P8080M07-001		
Revision No.:	A	