


60mm PAVING LAYERWORKS (light duty parking and driveways - cars)

SCALE 1 : 20

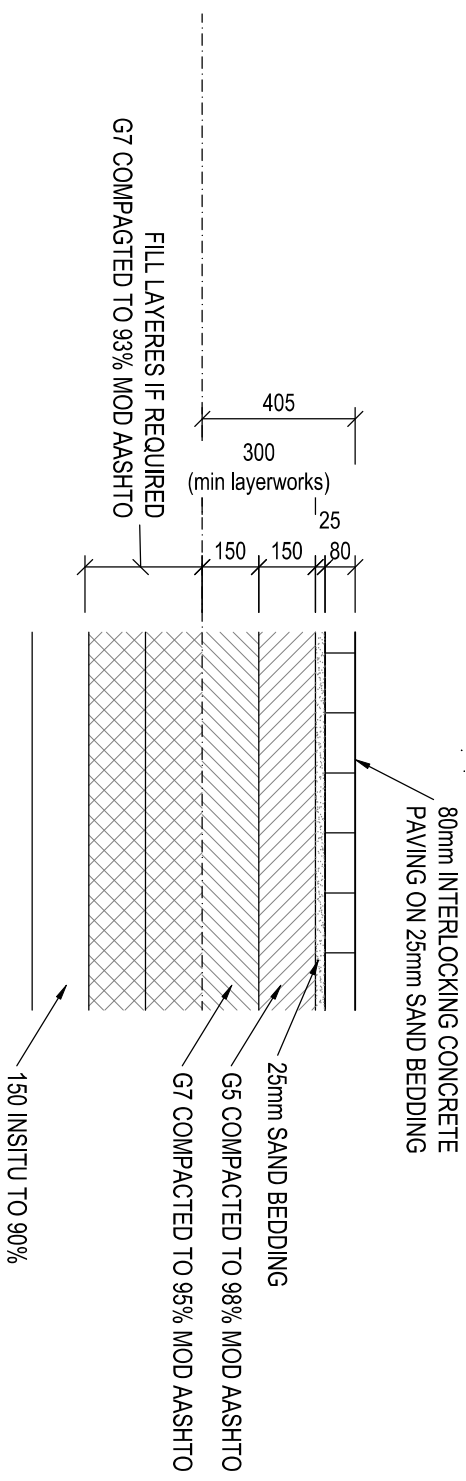

80mm PAVING LAYERWORKS (heavy duty - trucks and forklift areas)

SCALE 1 : 20