


FOR INFORMATION

SECTION C-C

SCALE 1:50

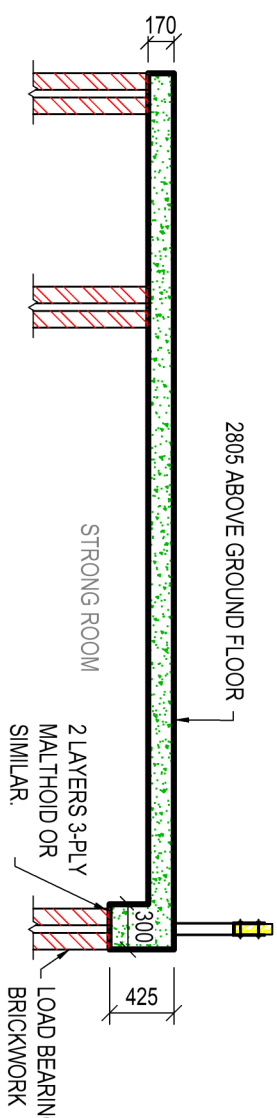

CITY ENGINEER / CLIENT REG. NO. DATE

AMENDMENTS CODE


DATE	INITIAL	REV	REVISION DESCRIPTION
2025/01/19	Z/R	A	ISSUE FOR INFORMATION
2025/10/30	TS	B	RING BEAMS UPDATED
2025/11/07	TS	C	COLUMNS DIMITED AND DETAILS ADDED
2025/11/12	TS	D	COLUMNS AND BEAM ADDED
2025/11/24	TS	E	COLUMNS AND SLAB ADDED

COPYRIGHT OF THIS DESIGN AND DRAWINGS IS RESERVED. SCALED DIMENSIONS ARE INVAILD. ALL DIMENSIONS & LEVELS TO BE VERIFIED ON SITE IMMEDIATELY. ALL BUILDING WORK TO BE IN COMPLIANCE WITH NATIONAL BUILDING REGULATIONS, SOUTH AFRICAN NATIONAL STANDARDS AND LOCAL AUTHORITY BY-LAWS.

ENGINEERING CONSULTANT: CIVIL & STRUCTURAL

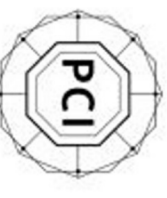

POWER CONSULTANCY
INTERNATIONAL
IN COLLABORATION WITH



bara
BARA ENGINEERING & CONSTRUCTION
PRIVATE LIMITED
REG. NO. 2015/0000000/000
BARA 23055

CLIENT

UFH

PROJECT

CONVERSION OF EXISTING CLINIC TO OFFICES, ALICE

DRAWING TITLE


RING BEAM LAYOUT AND DETAILS

APPROVED BY PCI

ENGINEER/TECHNOLOGIST REG. NO. DATE


SCALE	AS SHOWN	DESIGNED	AS
DATE	FEBRUARY 2025	DRAWN	Z/R
PAPER SIZE	A0	CHECKED	NMB
PROJECT NO.	PCI P0000	CLIENT PROJECT NO.	-
BARA 23055			

PCI : P0000/000/S/003
BARA : 25055/00/20/003

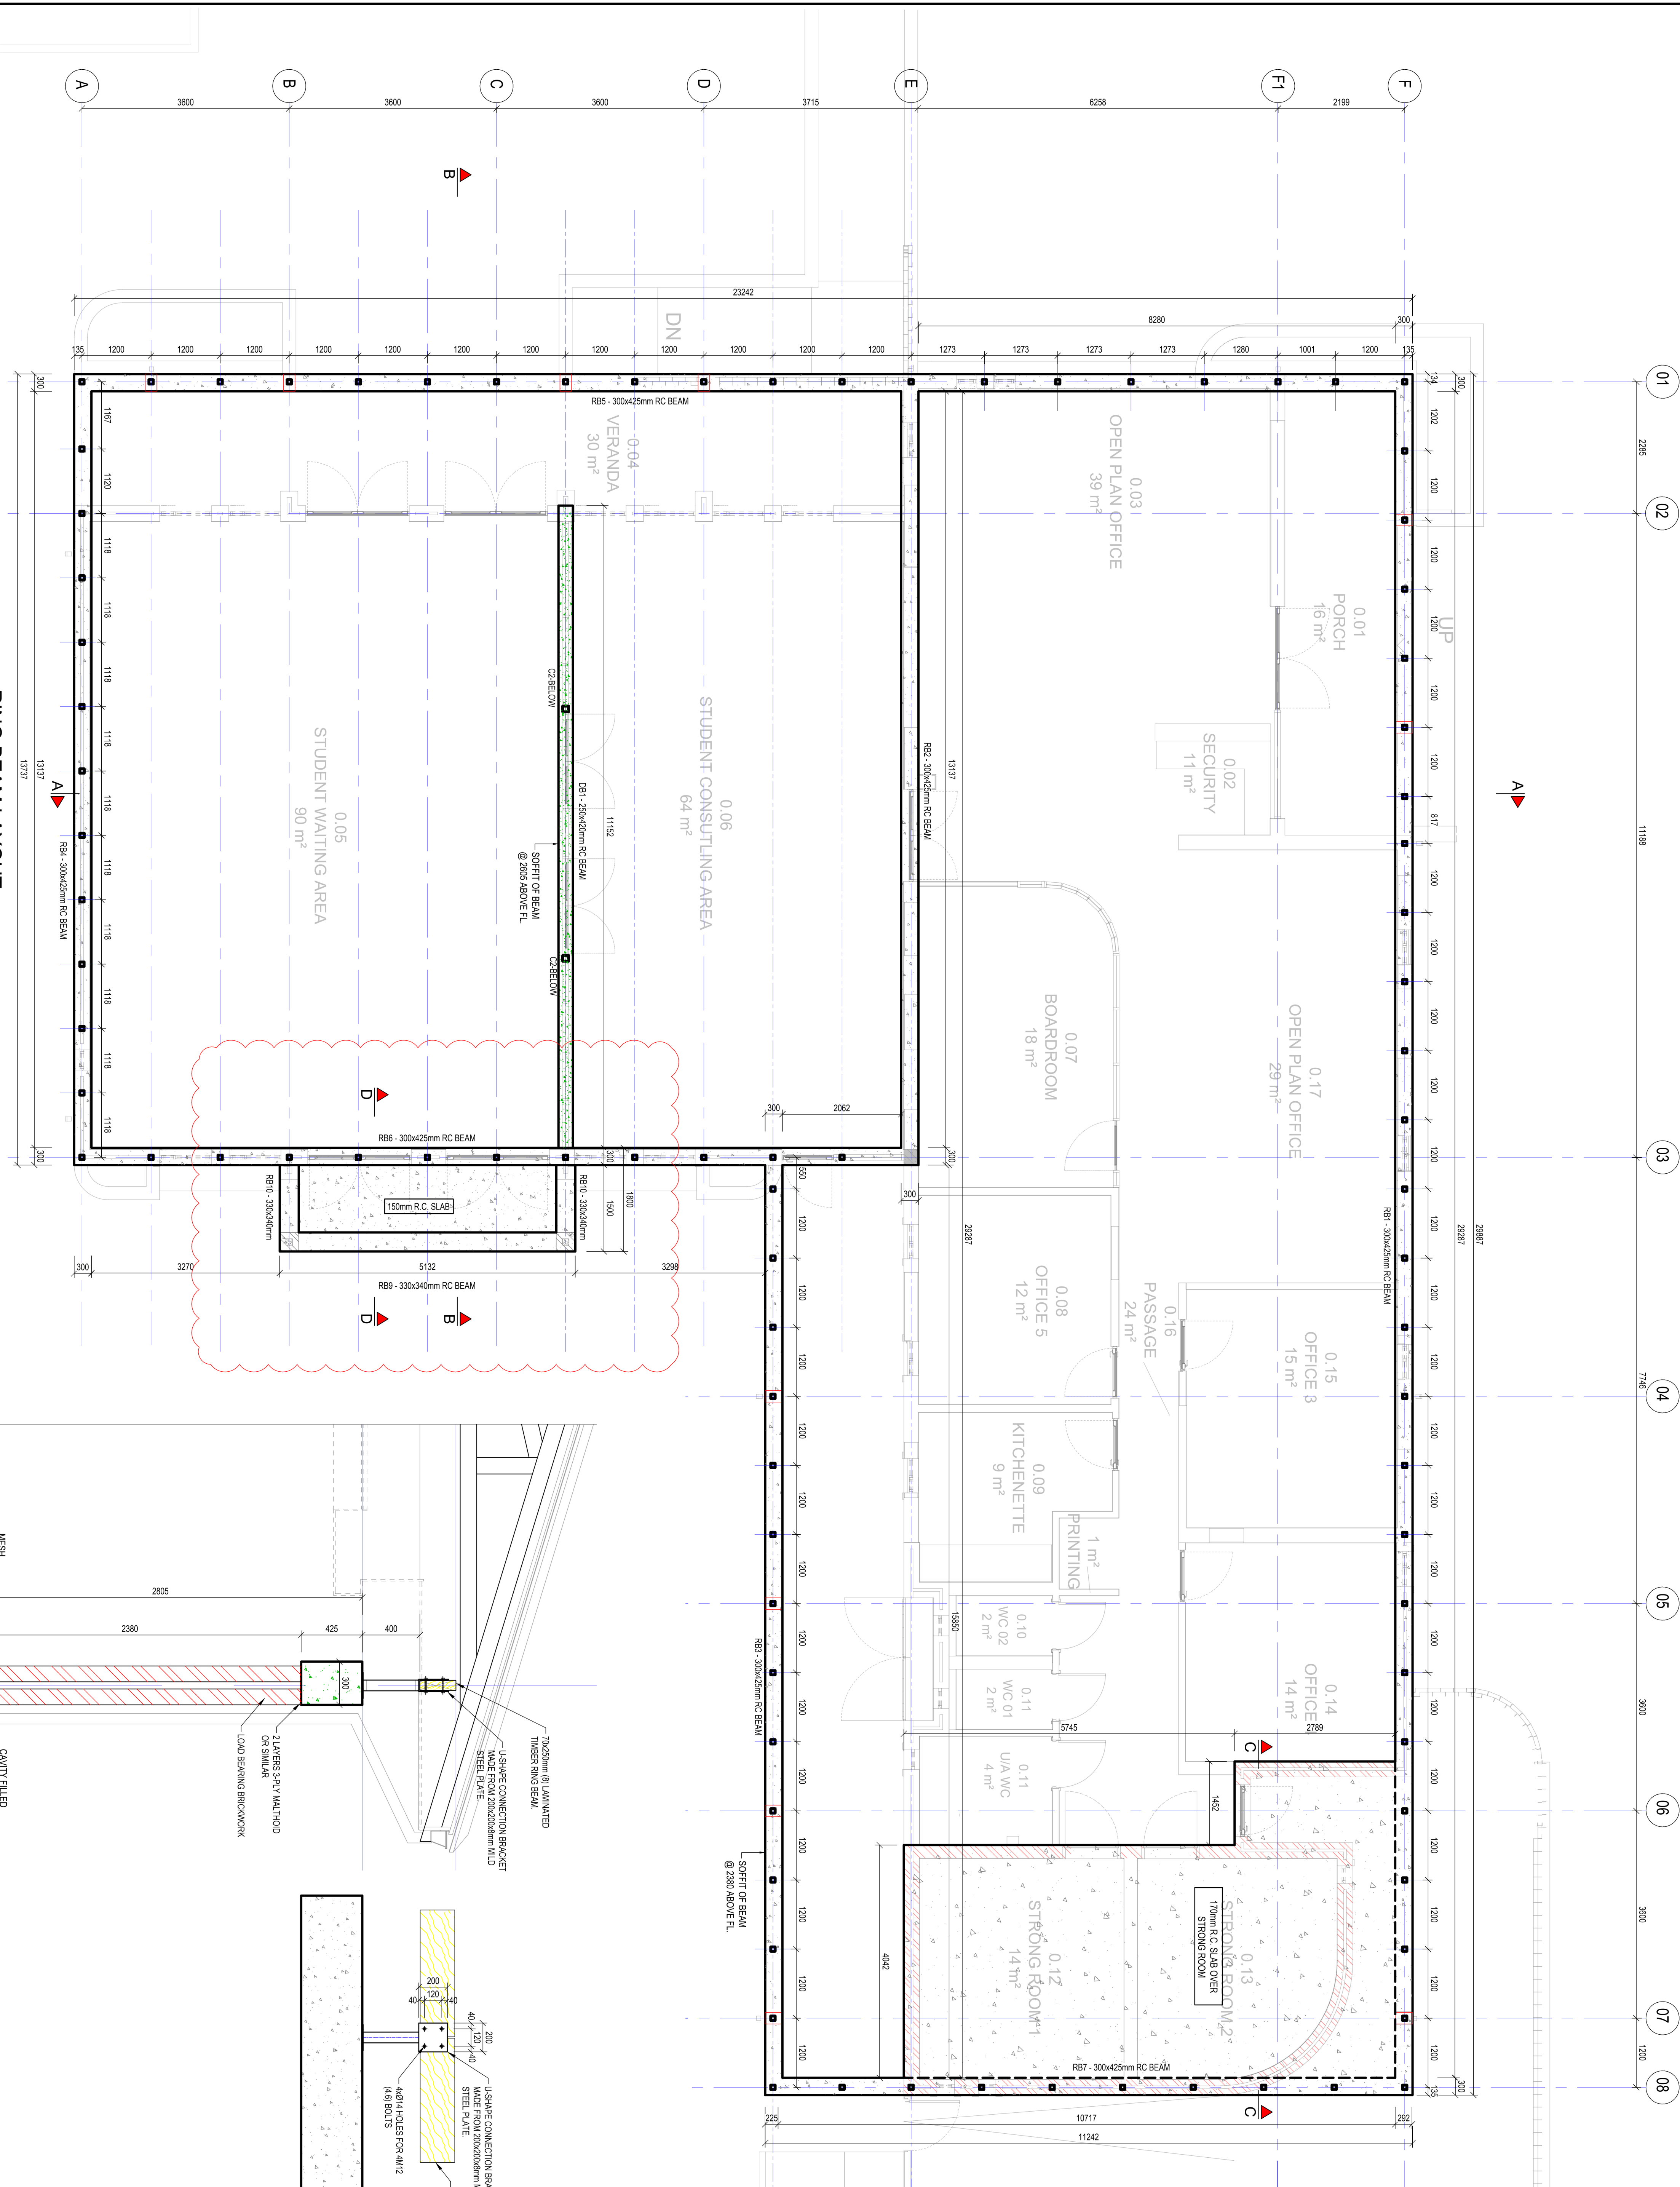

RING BEAM LAYOUT

SCALE 1:50

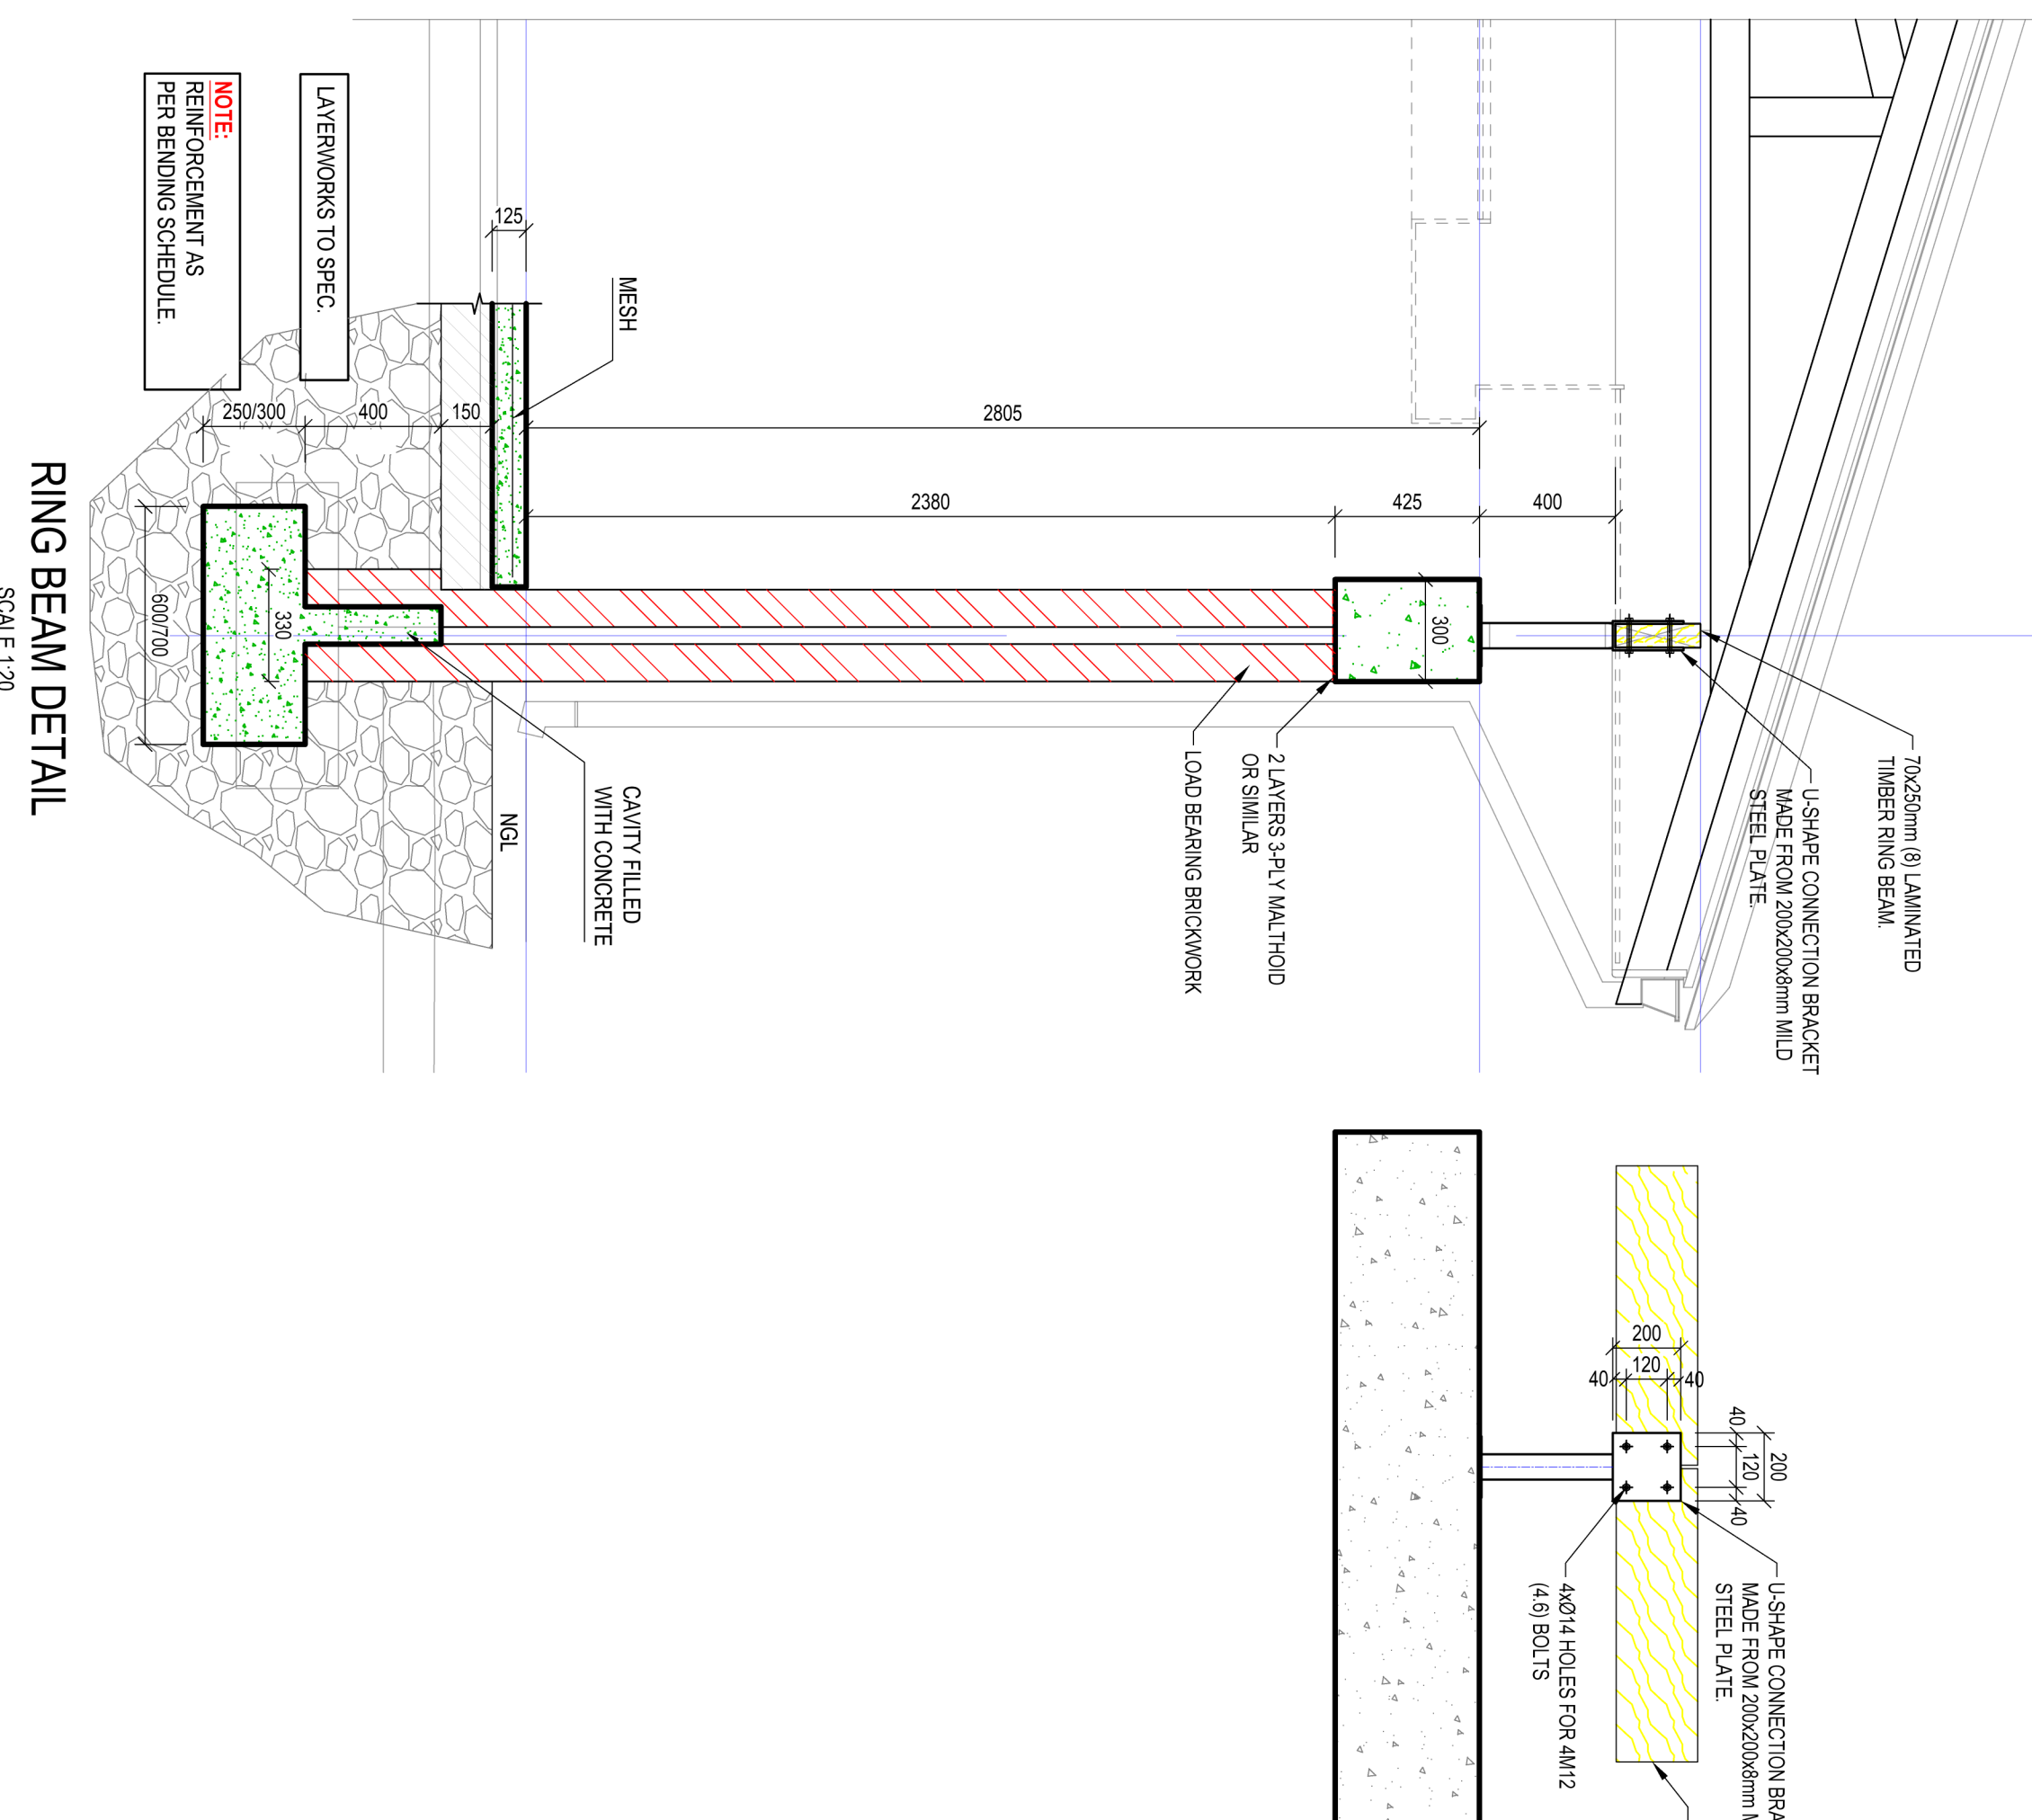


RING BEAM DETAIL

SCALE 1:20

BASEPLATE DETAIL

SCALE 1:5

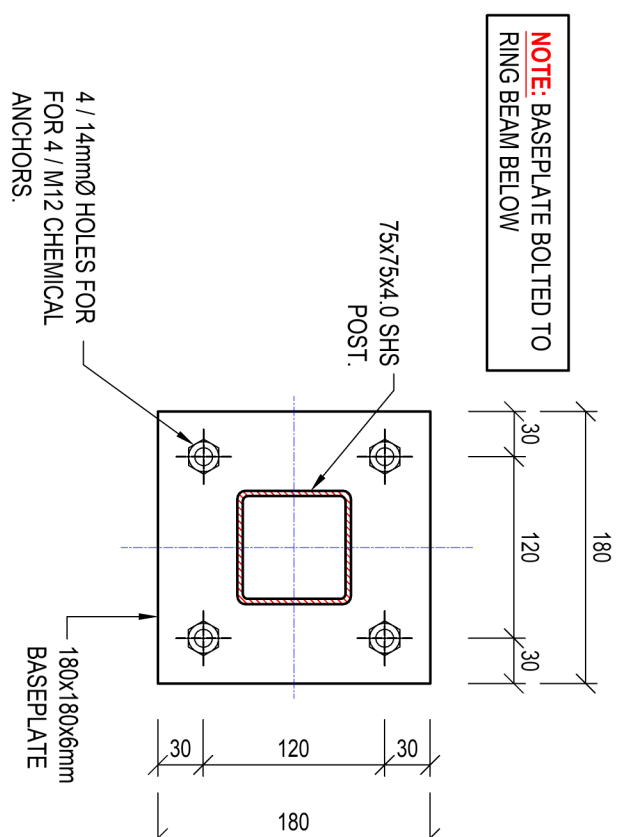

SECTION D-D

SCALE 1:25

